


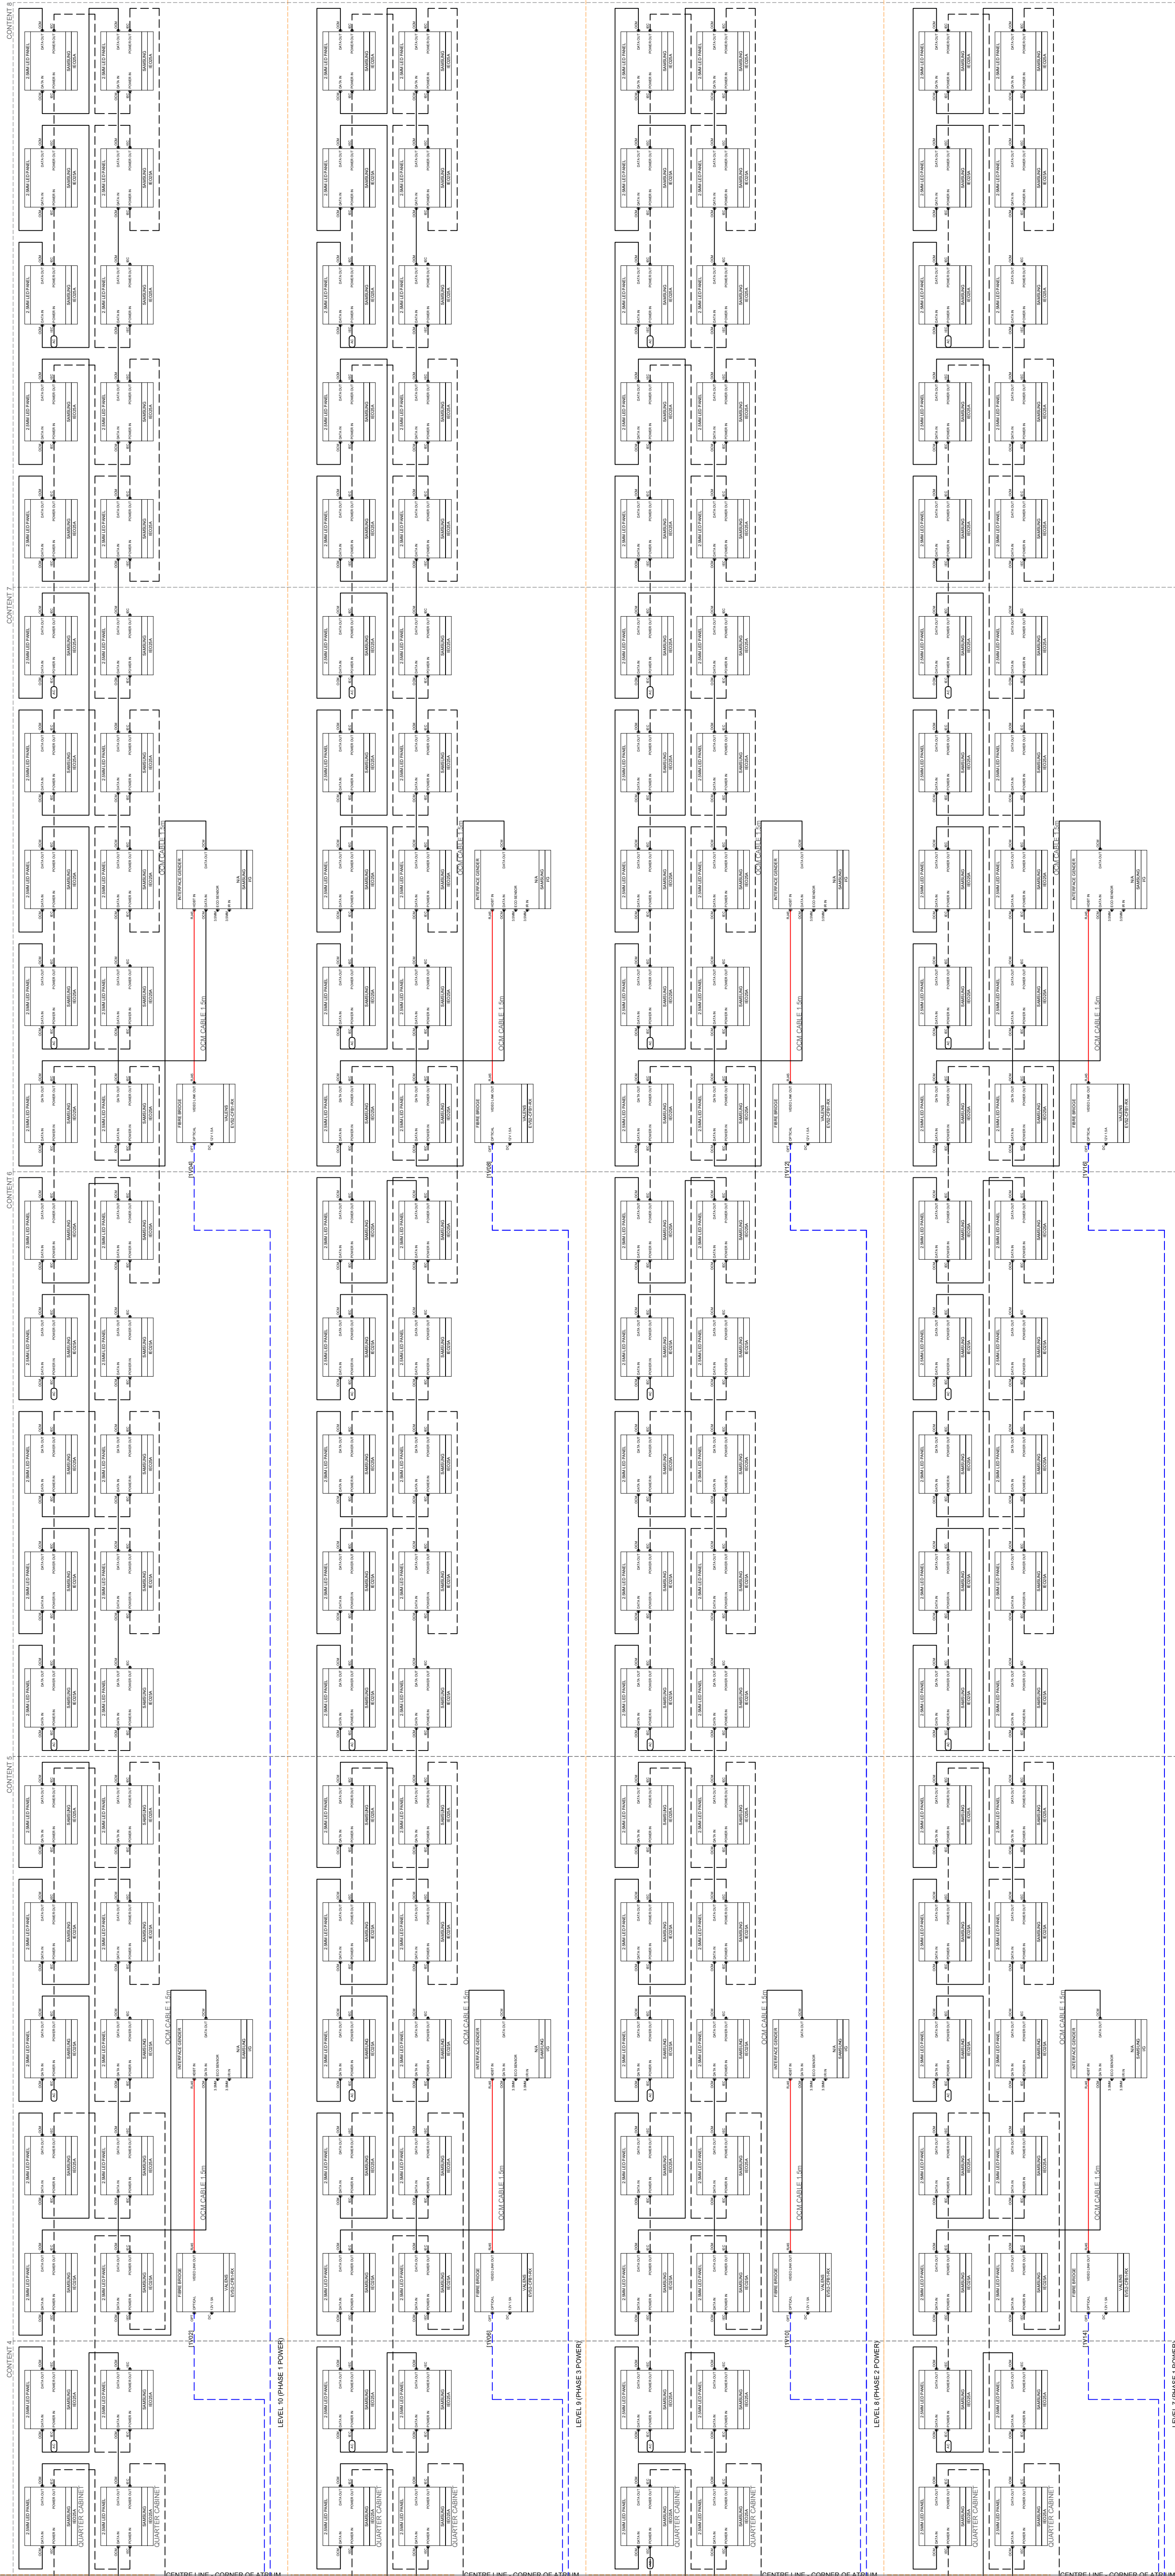

NOTE:

ALL CABLES TO BE NUMBERED WITH PERMANENT LABELS.

5M CABLE TAIL LENGTHS TO BE LEFT AT RACK LOCATIONS.

1M MINIMUM CABLE TAIL LENGTHS TO BE LEFT AT ALL OTHER POINTS UNLESS OTHERWISE STATED

DIMENSIONS, LOCATIONS AND CABLE ROUTES INDICATIVE ONLY. FINAL COORDINATION BY OTHERS.

LEGEND

- 2 CORE SPEAKER CABLE
- 4 CORE SPEAKER CABLE
- 2.5MM 4 CORE SPEAKER CABLE
- CAT 6 BLUE - TELEPHONE
- CAT 6 GREEN - DATA
- CAT 6 GREEN - DATA - AVB
- CAT 6 GREEN - DATA - DANTE
- CAT 6 GREEN - DATA - DS
- CAT 6 GREEN - DATA - IPTV
- CAT 6 GREEN - DATA - NVX
- CAT 6 GREEN - DATA - QLAN
- CAT 6 GREEN - DATA - VOIP
- CAT 6 GREEN - DATA - VC
- CAT 6 350 MHz - RED - AUDIO / VIDEO
- CAT 6 - YELLOW - CONTROL
- FST
- STARQUAD
- HDMI CABLE
- WF100 RF/SAT COAXIAL
- RGBHV CABLE
- SIAMESE CABLE
- HOME AUTOMATION CABLE
- 8G CABLE
- 6 CORE CONTROL
- FIBRE
- 3 CORE AND EARTH
- REVISION CLOUD
- 50 Ω LOW LOSS COAX CABLE
- 75 Ω COAX CABLE
- DMX CABLE
- DVI
- DISPLAYPORT
- USB 2.0
- USB 3.0

NOT FOR CONSTRUCTION

© Copyright. All rights to this drawing and its design are the property of SmartComm Ltd. Any use or duplication of this drawing is strictly prohibited without prior written permission of SmartComm Ltd.

Drawn By	EC	29/06/22
Checked By	GA	29/06/22
Issued By	GA	29/06/22

SCALE NOT TO SCALE

smartcomm
integrating technology with vision

SmartComm Ltd
3 Barrow Wells Court
Washington Road
Crayke Business Park
High Wycombe
Buckinghamshire
HP12 3PS
Tel: 0494 001 0004 470032
Fax: 44 (0) 1494 472664
E-mail: info@smartcomm.co.uk
Web: www.smartcomm.co.uk

Rev	Description	Date	Name
P01	For Approval	10/06/22	EC
P02	Update Description	29/06/22	EC

Barclays 1CP
Video Wall East
AV Schematic

BPLTF-SMC-ZZ-ZZ-SC-X-02004